

THIS DRAWING IS UNPUBLISHED. RELEASED FOR PUBLICATION -,- .
© COPYRIGHT - By - ALL RIGHTS RESERVED.

REVISIONS					
P	LTR	DESCRIPTION	DATE	DWN	APVD
	A2	REVISED PER ECO-16-018632	05APR2017	SK	PO

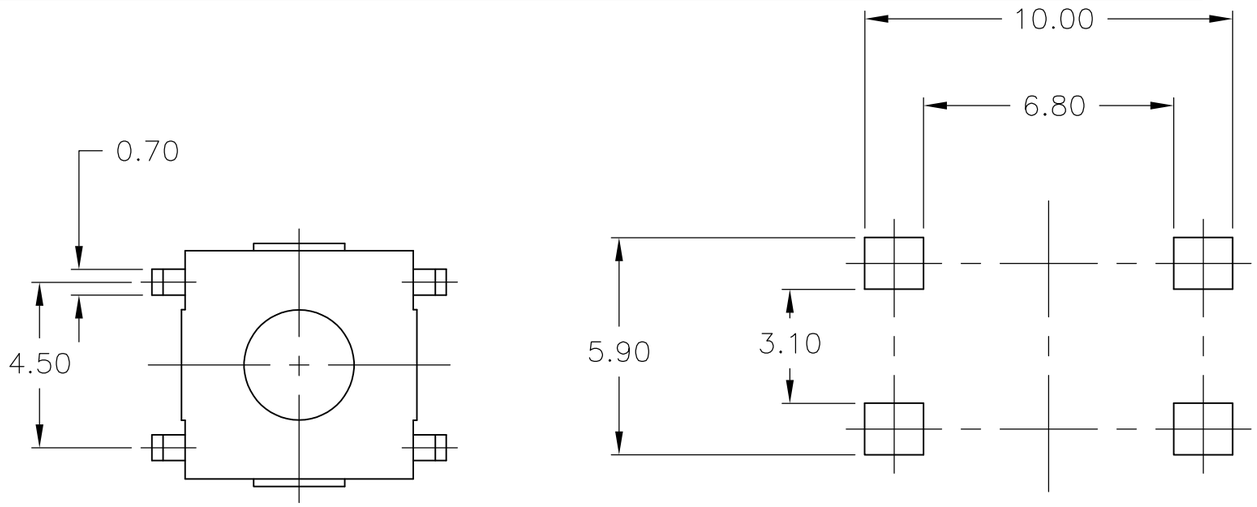

P C B LAND DIMENSION

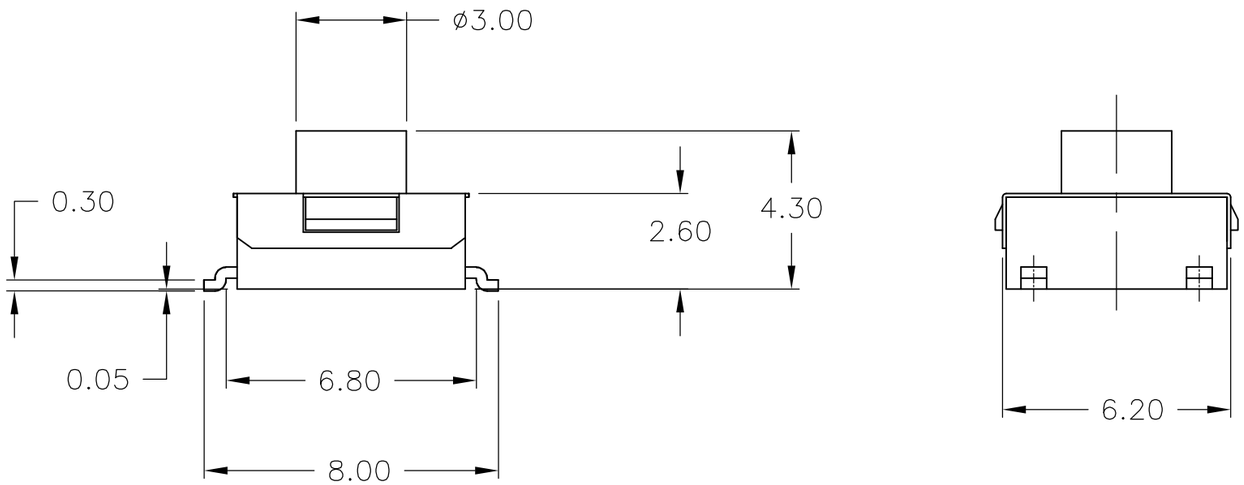

() - INDICATES MOMENTARY POSITION		
CIRCUIT CHARACTERISTICS		
CONTACT POSITION		CIRCUIT DIAGRAM
OFF	(ON) 1-3 2-4	1 2 3 4

SPECIFICATIONS:

MATERIALS:
CASE, NYLON 46 UL94 V-0, IVORY
ACTUATOR, NYLON PA6T UL94V-0, PINK FINISH
COVER, COPPER ALLOY, TIN FINISH
TERMINAL/FIXED CONTACT, COPPER ALLOY-SILVER FINISH
MOVING CONTACT, STAINLESS STEEL-SILVER FINISH

ELECTRICAL:
MAX CONTACT RATING, 50MILLIAMP@24V DC
MIN CONTACT RATING, 1MICROAMP@1V DC
CONTACT RESISTANCE, 100 MILLIOHMS MAX
INSULATION RESISTANCE, 100 MEGOHM MIN.
DIELECTRIC STRENGTH, 500 V AC FOR 1 MINUTE
LIFE EXPECTANCY, 1,000,000 CYCLES

MECHANICAL:
ACTUATION FORCE, 260 +/-50GF
ACTUATION TRAVEL, 0.25 +0.20/-0.10
LIFE EXPECTANCY, 1,000,000, (2 CYCLES PER SECOND AND 150% ACTUATION FORCE)

ENVIRONMENTAL:
OPERATING TEMPERATURE, -40 TO +105° C
STORAGE TEMPERATURE, -40 TO +105° C
SOLDERABILITY, EIA-RS-186-9E, OR MIL-STD-202F
RESISTANCE TO SOLDER HEAT, 260° C FOR 10SEC-PER 109-201, CONDITION B
1.NO CHANGE IN INITIAL ELECTRICAL AND MECHANICAL CHARACTERISTICS

NOTES:

1 ALL MATERIALS AND FINISHES SHALL COMPLY WITH EU DIRECTIVE 2002/95/EC OF 27JAN2003 (ROHS)

	PACKAGING	LIFE CYCLE	ACTUATOR COLOR	ACTUATION FORCE	T&B P/N	TE P/N
	TAPE AND REEL	1,000,000	PINK	260 +/-50g	FSM4LPASTR	1977264-2
OBSOLETE	~~BULK~~	~~1,000,000~~	~~PINK~~	~~260 +/-50g~~	~~FSM4LPAS~~	~~1977264-1~~

THIS DRAWING IS A CONTROLLED DOCUMENT.

DIMENSIONS: mm

TOLERANCES UNLESS OTHERWISE SPECIFIED:
0 PLC ± -
1 PLC ± -
2 PLC ± 0.30
3 PLC ± -
4 PLC ± -
ANGLES ± -

MATERIAL -
FINISH -

DWN M.BINNER 24JAN08
CHK M.SARVER 24JAN08
APVD M.SARVER 24JAN08
PRODUCT SPEC -
APPLICATION SPEC -
WEIGHT 0

TE Connectivity

NAME
TACTILE SWITCH 6X6mm
LOW PROFILE,
SURFACE MOUNT

SIZE	CAGE CODE	DRAWING NO	RESTRICTED TO
A3	00779	C-1977264	-


CUSTOMER DRAWING | SCALE 6:1 | SHEET 1 OF 2 | REV A2

THIS DRAWING IS UNPUBLISHED. RELEASED FOR PUBLICATION –,– .
© COPYRIGHT – By – ALL RIGHTS RESERVED.

REVISIONS

P	LTR	DESCRIPTION	DATE	DWN	APVD
	–	SEE SHEET 1	–	—	—


* THE DIMENSION OF CARRIER TAPE, COVER TAPE AND REEL *

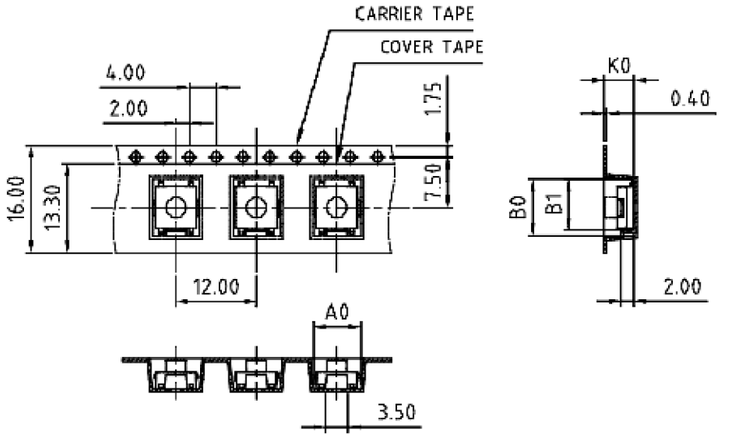



* DIMENSION

구 분	치 수
A0	7.00mm
B0	8.40mm
B1	7.55mm
K0	4.50mm


* THE DIRECTION OF PILOT HOLES *

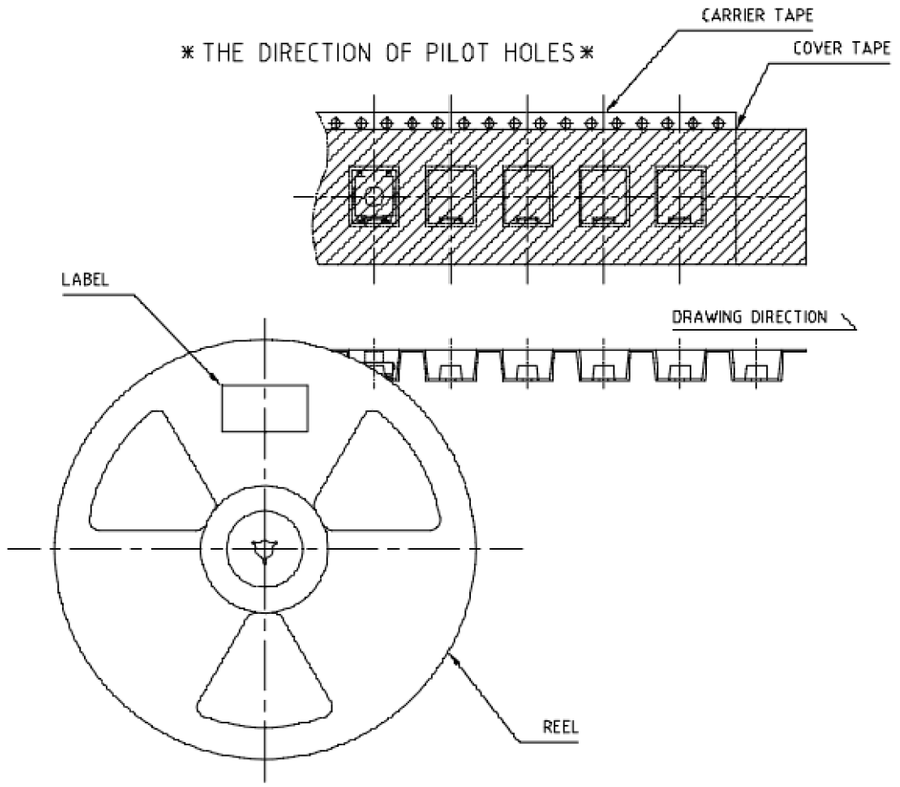

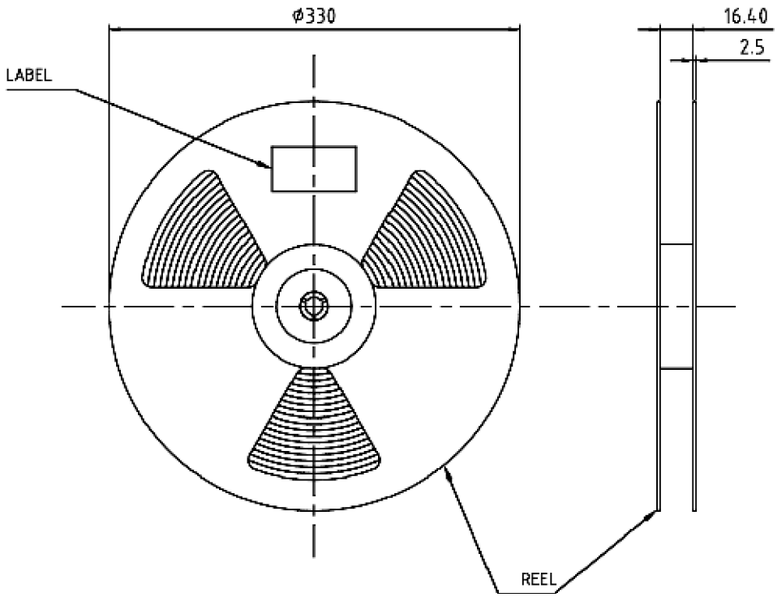

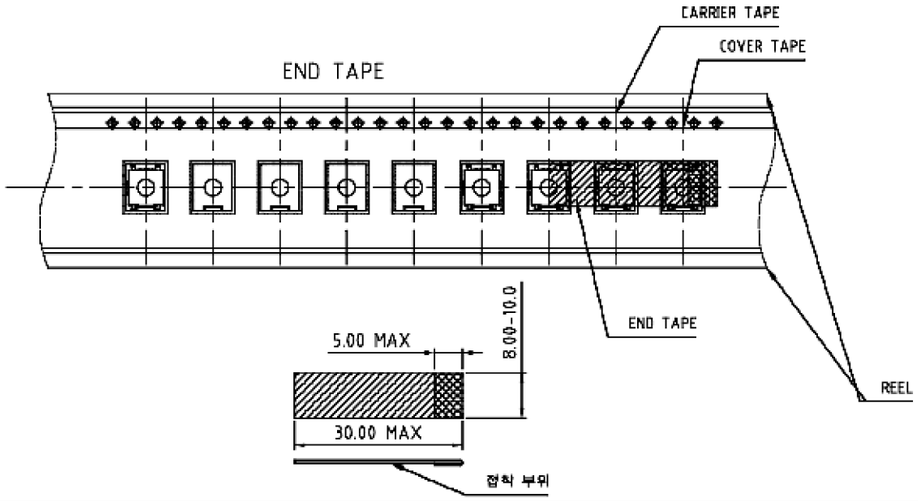

* THE SPECIFICATION FOR PACKAGING *

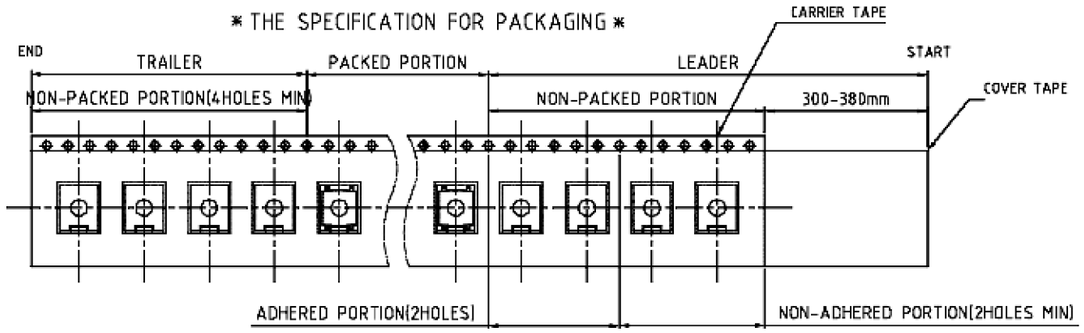

THIS DRAWING IS A CONTROLLED DOCUMENT.

DIMENSIONS: mm

TOLERANCES UNLESS OTHERWISE SPECIFIED:
0 PLC ± –
1 PLC ± –
2 PLC ± 0.30
3 PLC ± –
4 PLC ± –
ANGLES ± –

MATERIAL –

FINISH –

DWN	M.BINNER	24JAN08
CHK	M.SARVER	24JAN08
APVD	M.SARVER	24JAN08
PRODUCT SPEC	—	
APPLICATION SPEC	—	
WEIGHT	–	

TE Connectivity

NAME
TACTILE SWITCH 6X6mm
LOW PROFILE,
SURFACE MOUNT

SIZE	CAGE CODE	DRAWING NO	RESTRICTED TO
A3	00779	C-1977264	—

CUSTOMER DRAWING | SCALE 6:1 | SHEET 2 OF 2 | REV A2